


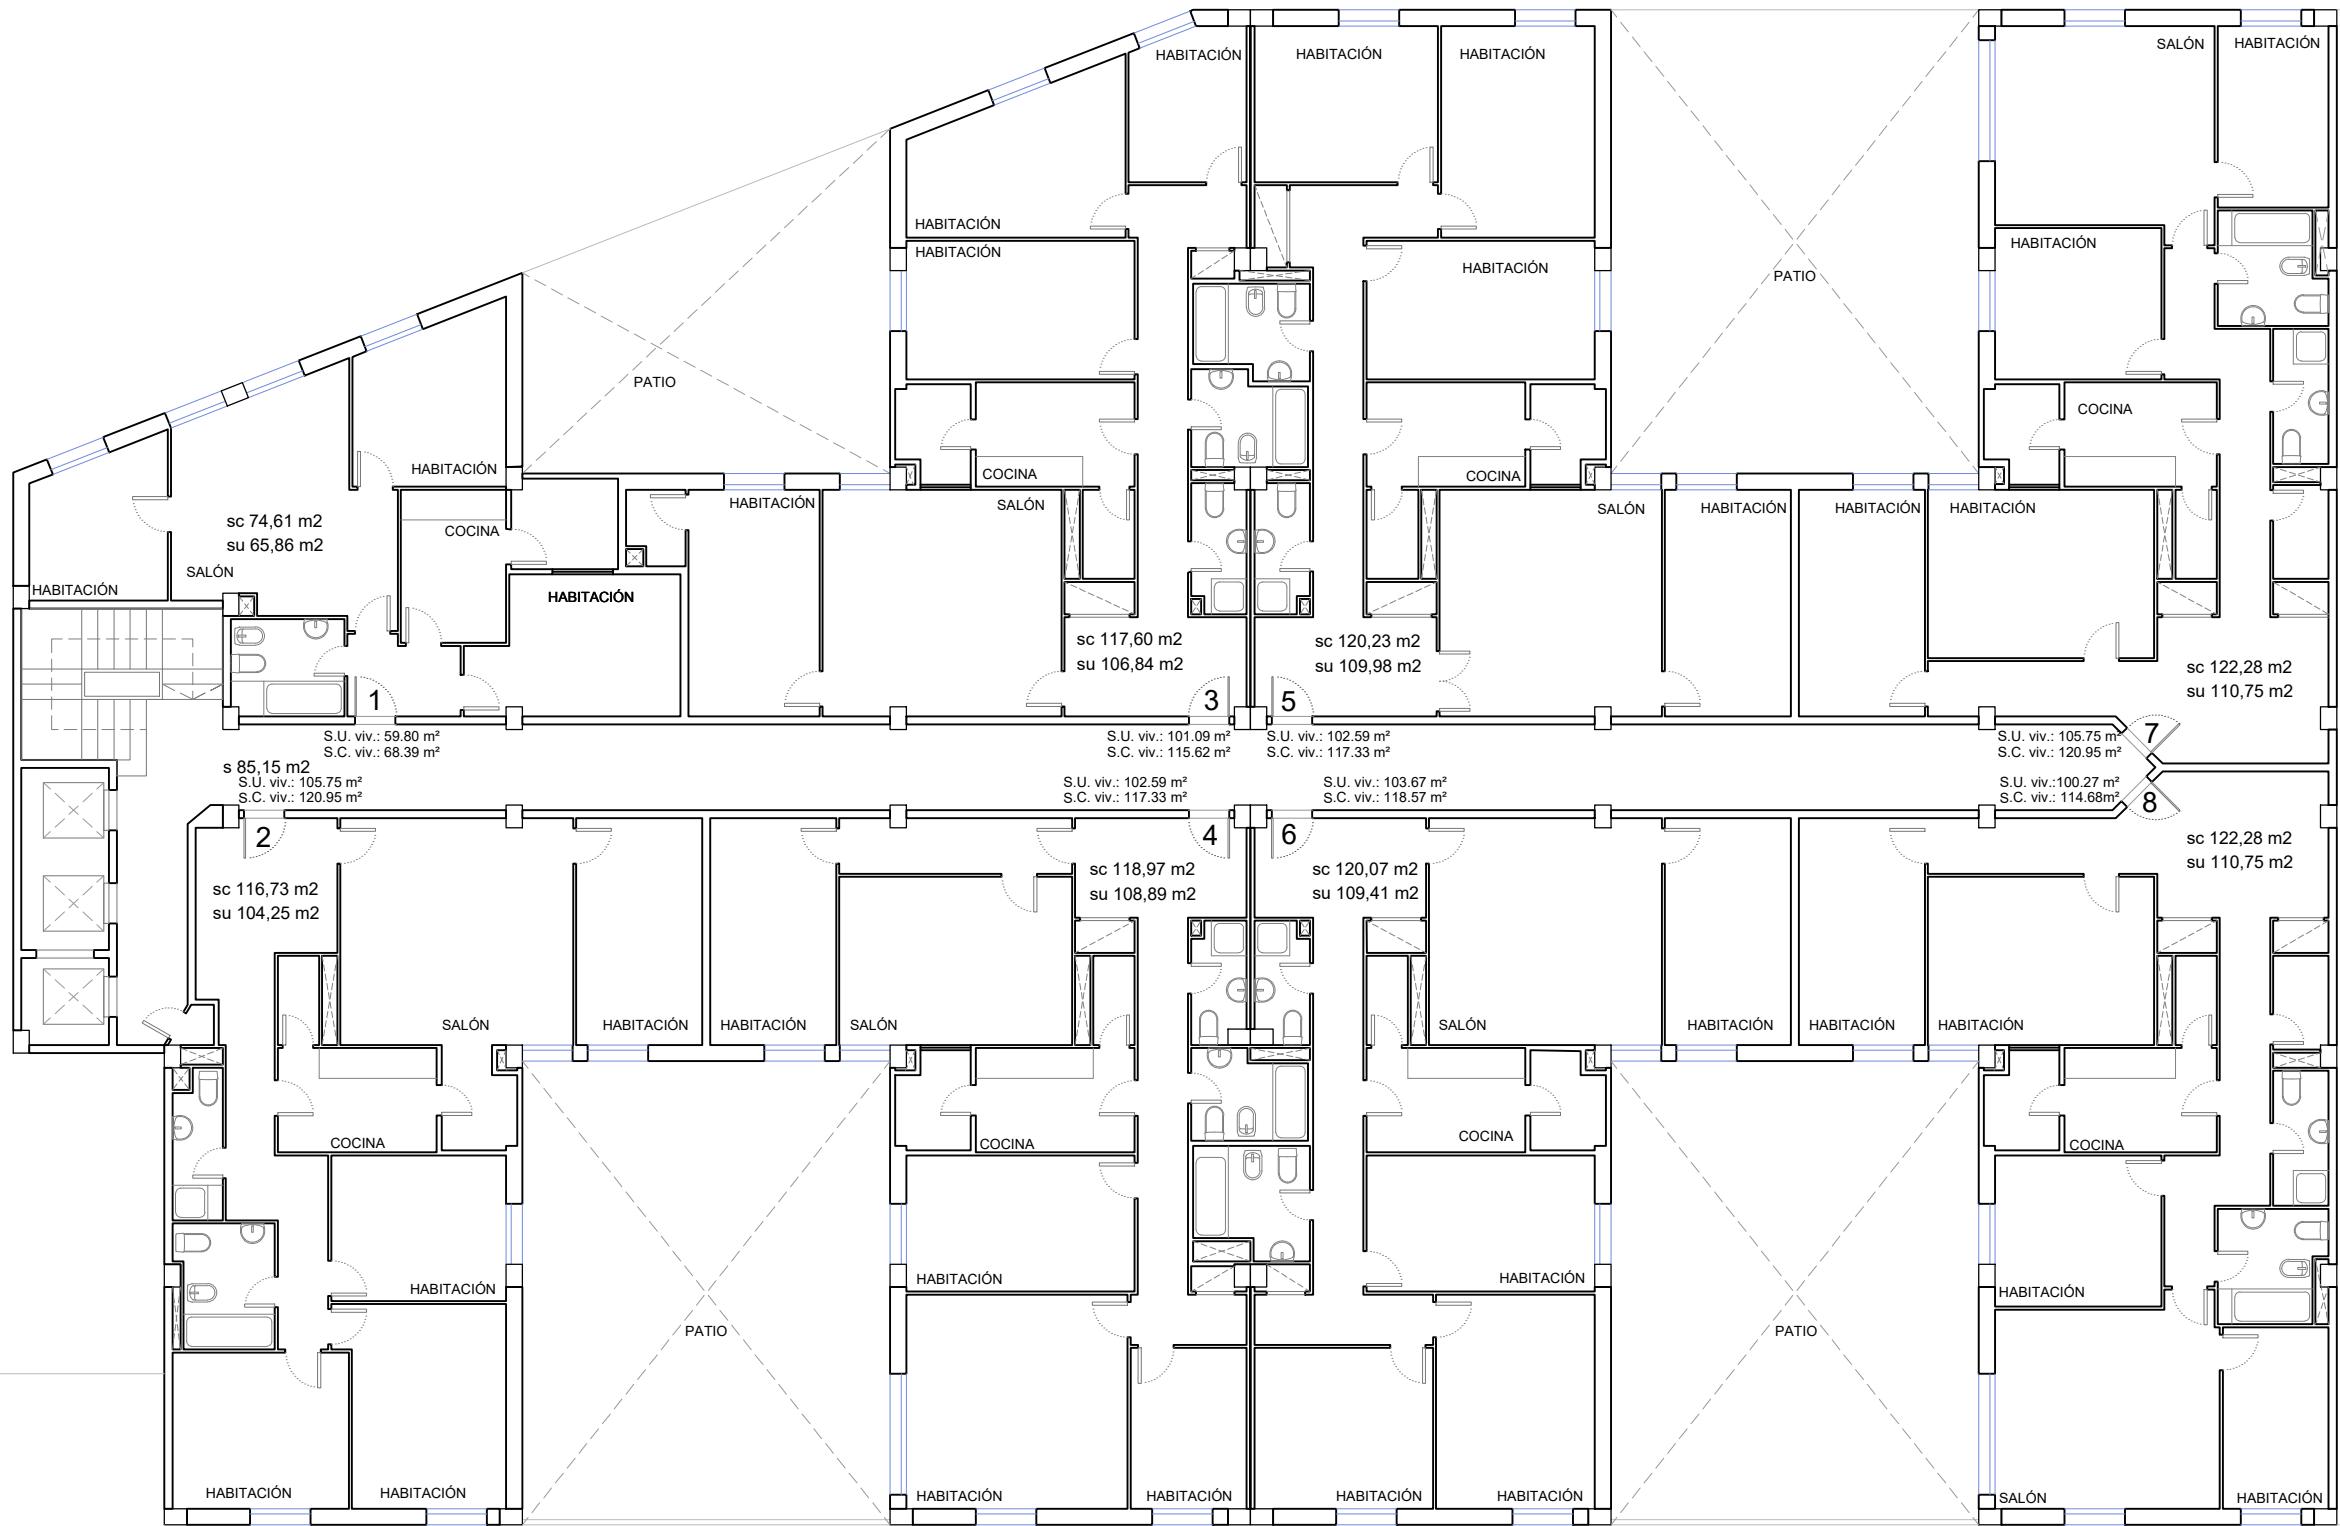

SUPERFICIE CONSTRUIDA 997,92 m2

PLANTA TIPO_VIVIENDAS

CUADRO RESUMEN DE SUPERFICIES		
PLANTA	TIPOLOGÍA	SUP. CONST. (m²)
TIPO (2ª, 3ª, 4ª, 5ª, 6ª, 7ª Y 8ª)	VIVIENDA	893,82
	ZZ. CC.	128,46
TOTAL P. TIPO		1.022,28

CUADRO DE SUPERFICIES					
PLANTA TIPO	1	VIVIENDA	59,80	68,39	9,83
	2	VIVIENDA	105,75	120,95	17,38
	3	VIVIENDA	101,09	115,62	16,61
	4	VIVIENDA	102,59	117,33	16,87
	5	VIVIENDA	102,59	117,33	16,87
	6	VIVIENDA	103,67	118,57	17,04
	7	VIVIENDA	105,75	120,95	17,38
	8	VIVIENDA	100,27	114,68	16,48
TOTAL PLANTA TIPO			781,51	893,82	128,46
			1.022,28		

LEVANTAMIENTO DE EDIFICIO DESTINADO A VIVIENDAS, LOCALES, OFICINAS Y GARAJES
SITUACION
CALLE GENERAL ELORZA, 25 - OVIEDO
PROPIEDAD
VERSO ESPACIO RESIDENCIAL S.L.

PLANO: ESTADO ACTUAL
PLANTA TIPO (2ª, 3ª, 4ª, 5ª, 6ª, 7ª Y 8ª)

Nº PLANO:
A04

FECHA:
ENERO 2022

ESCALA:
1/150